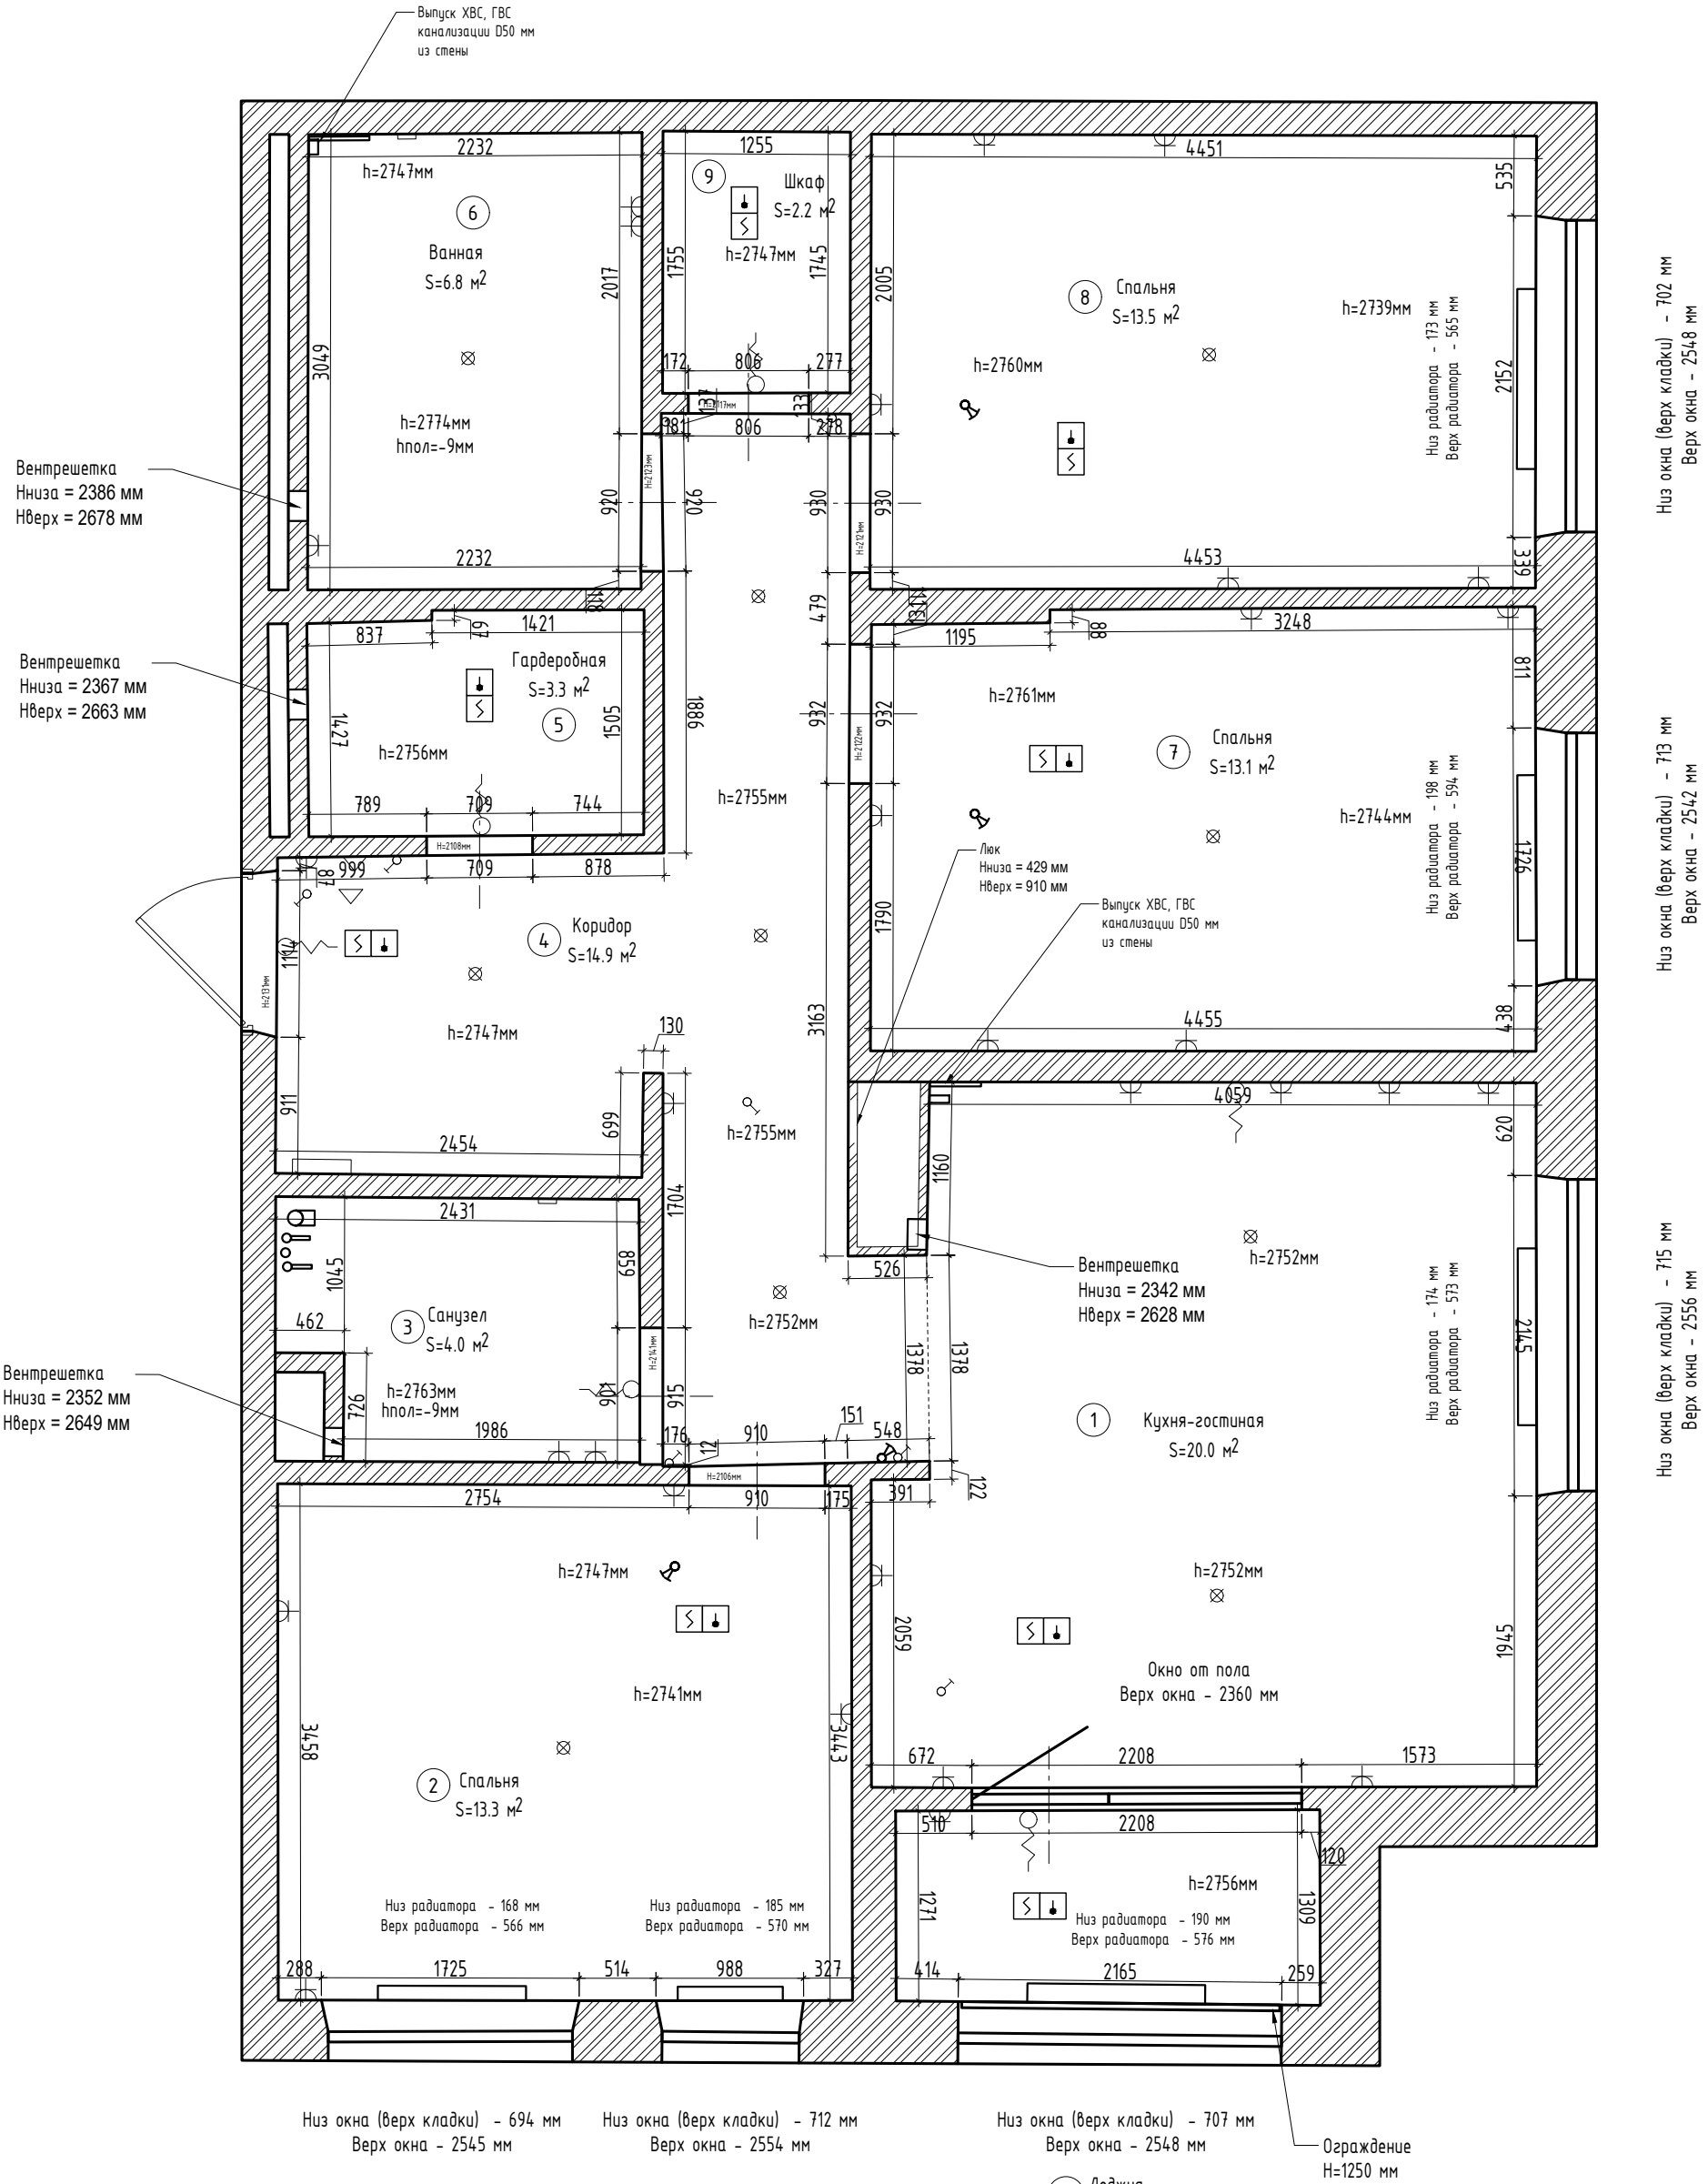


СПЕЦИФИКАЦИЯ ПОМЕЩЕНИЙ

№ п/п	НАИМЕНОВАНИЕ ПОМЕЩЕНИЯ	ПЛОЩАДЬ, м2
1	Кухня-гостиная	20.00
2	Спальня	13.26
3	Санузел	3.97
4	Коридор	14.94
5	Гардеробная	3.33
6	Ванная	6.81
7	Спальня	13.07
8	Спальня	13.51
9	Шкаф	2.20
10	Лоджия	3.66
ИТОГО:		94.75


Центр электрооборудования соответствует центру подрозетника (по горизонтали и по вертикали).

Дымовой и тепловой пожарные извещатели установлены попарно. Их совместный центр на чертеже соответствует фактическому центру их совместной установка в квартире.

Розетки, выпуски кабеля и прочее оборудование и коммуникации нанесены с привязкой к помещению. Недостающие размеры можно снять с чертежа.

На момент замера стены оштукатурены, стяжка залита.

Обмерный план	адрес: Республика Башкортостан, г. Уфа ЖК «Бионика Парк», улица 50 лет СССР, 39	дата обмера	8 917 750 63 16 amn84@bk.ru Замеры. Чертежи. Автоматизация типовых задач в AutoCad

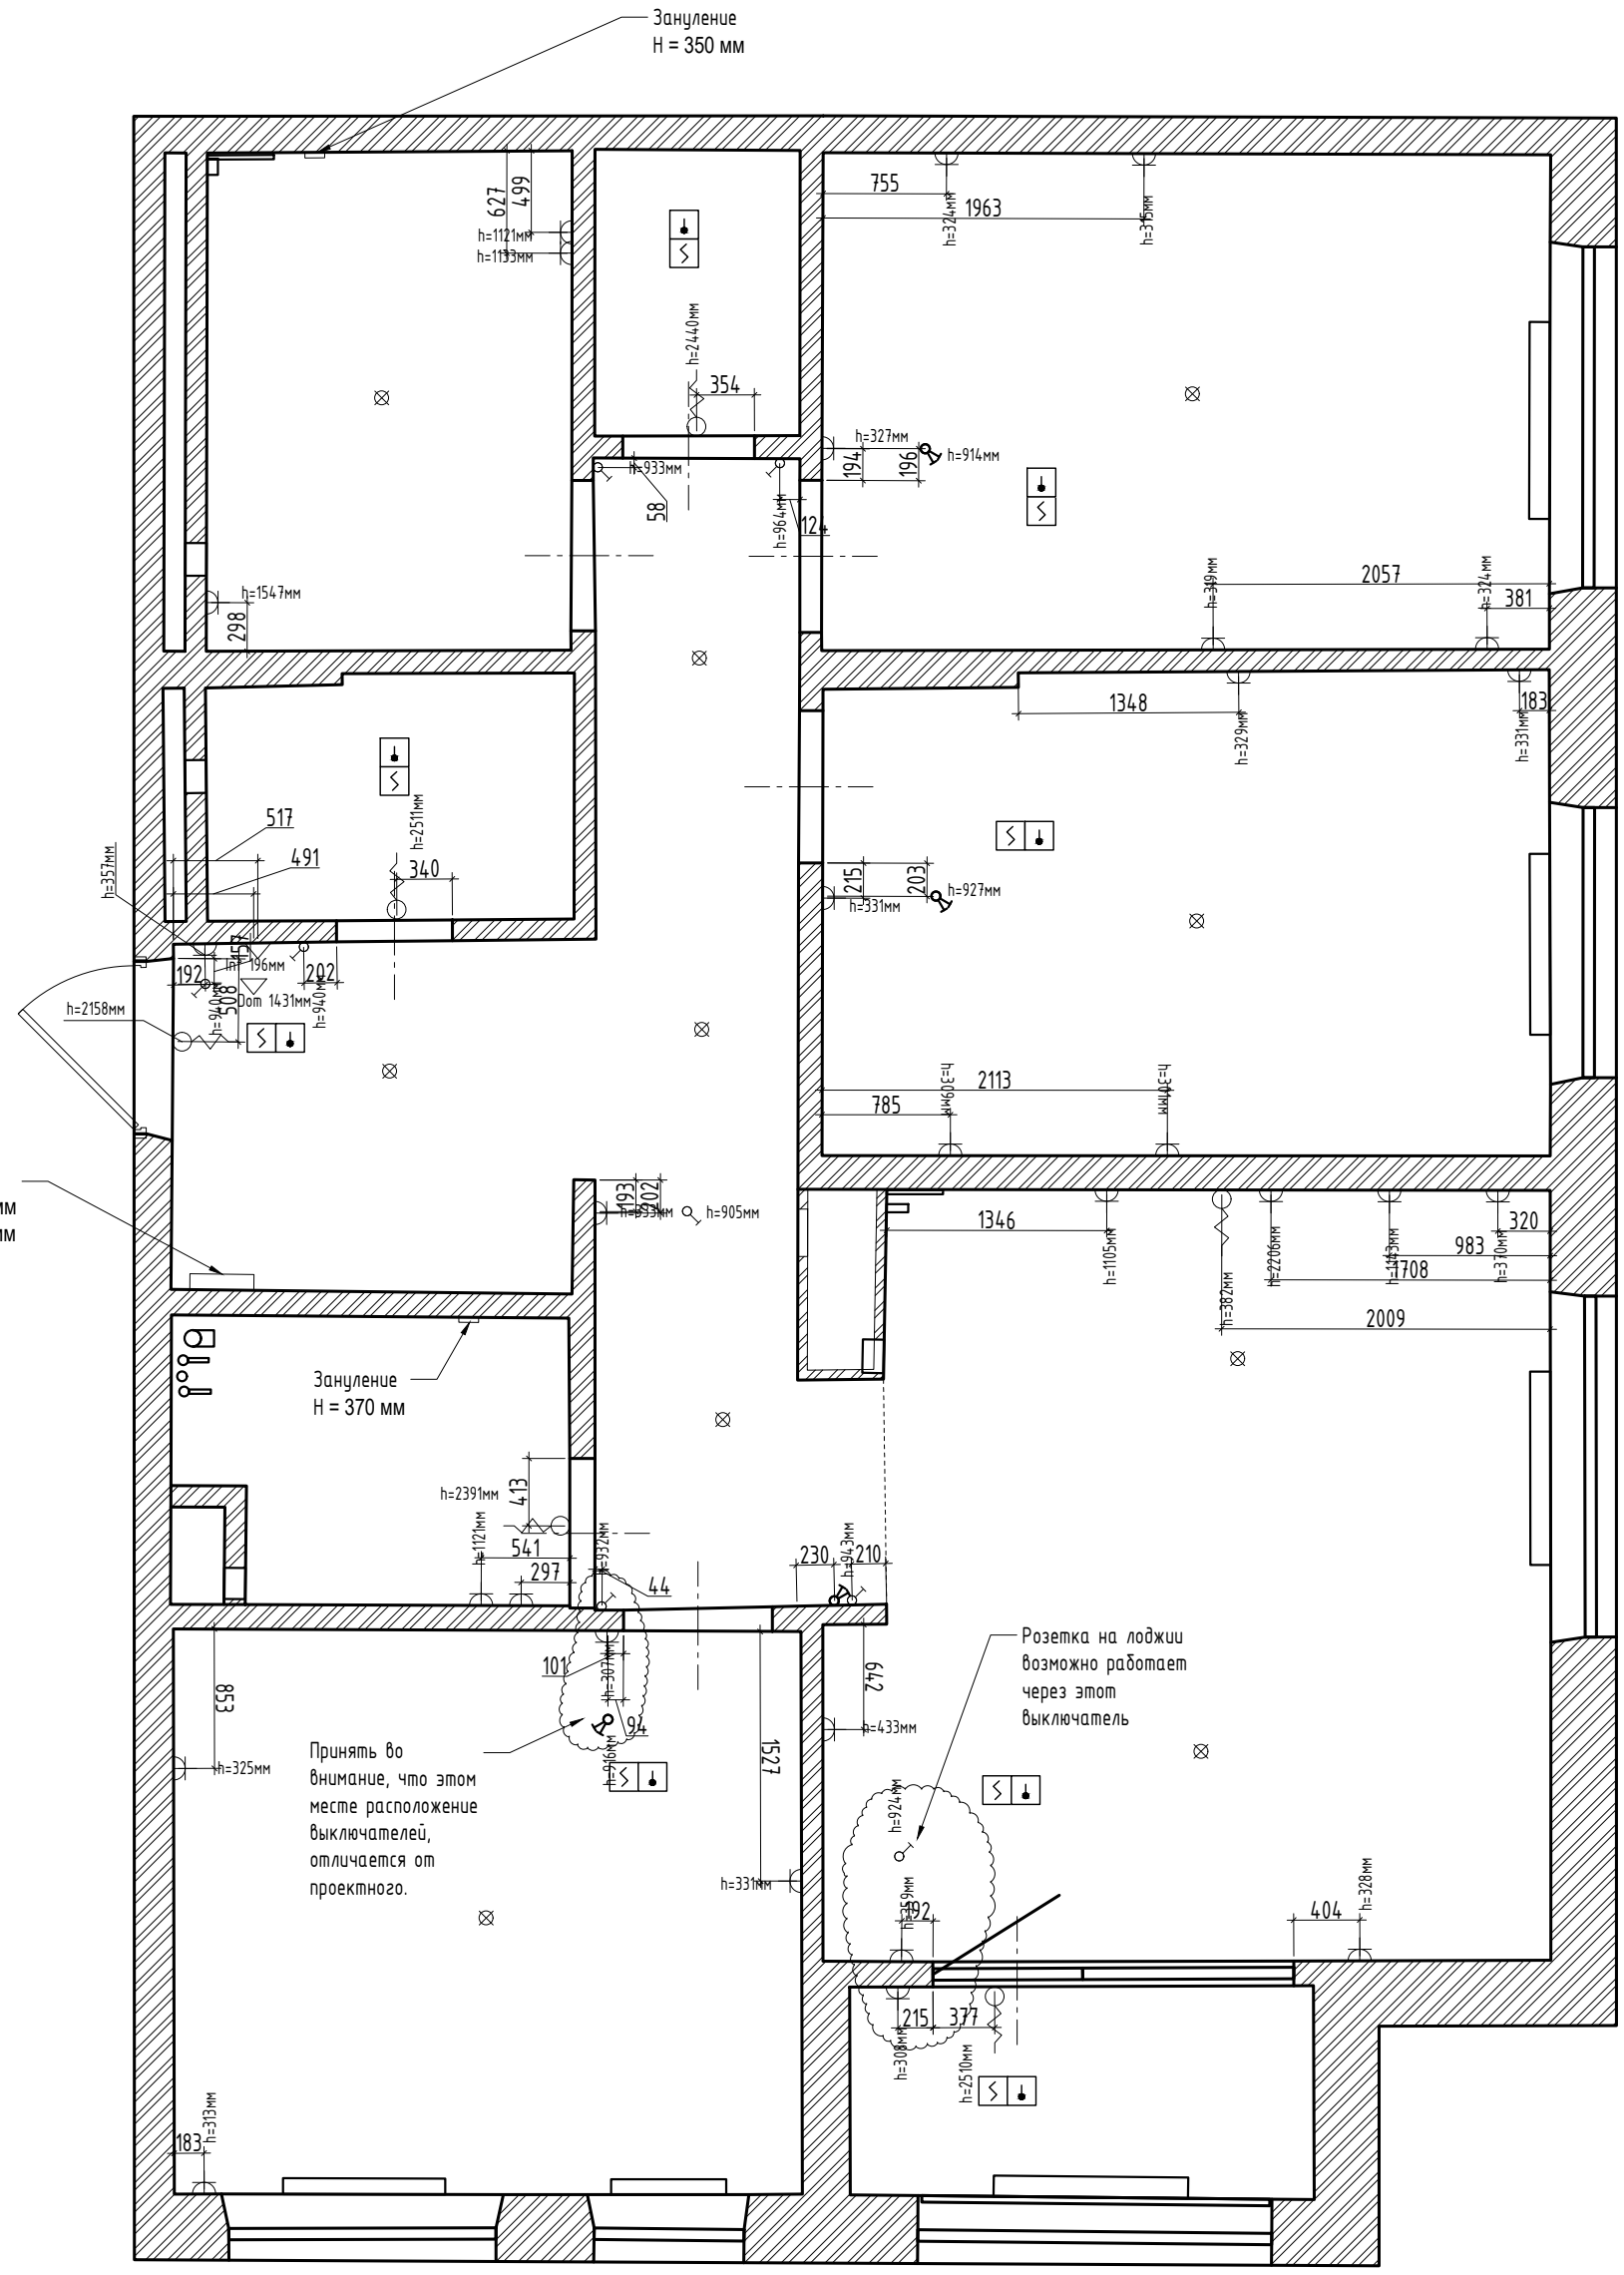

СПЕЦИФИКАЦИЯ ПОМЕЩЕНИЙ

№ п/п	НАИМЕНОВАНИЕ ПОМЕЩЕНИЯ	ПЛОЩАДЬ, м2
1	Кухня-гостиная	20.00
2	Спальня	13.26
3	Санузел	3.97
4	Коридор	14.94
5	Гардеробная	3.33
6	Ванная	6.81
7	Спальня	13.07
8	Спальня	13.51
9	Шкаф	2.20
10	Лоджия	3.66
ИТОГО:		94.75

Дымовой пожарный извещатель

Тепловой пожарный извещатель

Патрон подвесной

Выпуск кабеля

Выключатель одноклавишный скрытой установки

Выключатель двухклавишный скрытой установки

Розетка 1 постовая скрытой установки

Int — Распределительная коробка сети Intertet

Dom — Распределительная коробка сети для домофона

Центр электрооборудования соответствует центру подрозетника (по горизонтали и по вертикали).

Дымовой и тепловой пожарные извещатели установлены попарно. Их совместный центр на чертеже соответствует фактическому центру их совместной установка в квартире.

Розетки, выпуски кабеля и прочее оборудование и коммуникации нанесены с привязкой к помещению. Недостающие размеры можно снять с чертежа.

На момент замера стены оштукатурены, стяжка залита.

Обмерный план	Электроустановочные изделия	адрес: Республика Башкортостан, г. Уфа ЖК «Бионика Парк», улица 50 лет СССР, 39.	дата обмера	8 917 750 63 16 amn84@bk.ru Замеры. Чертежи. Автоматизация типовых задач в AutoCad