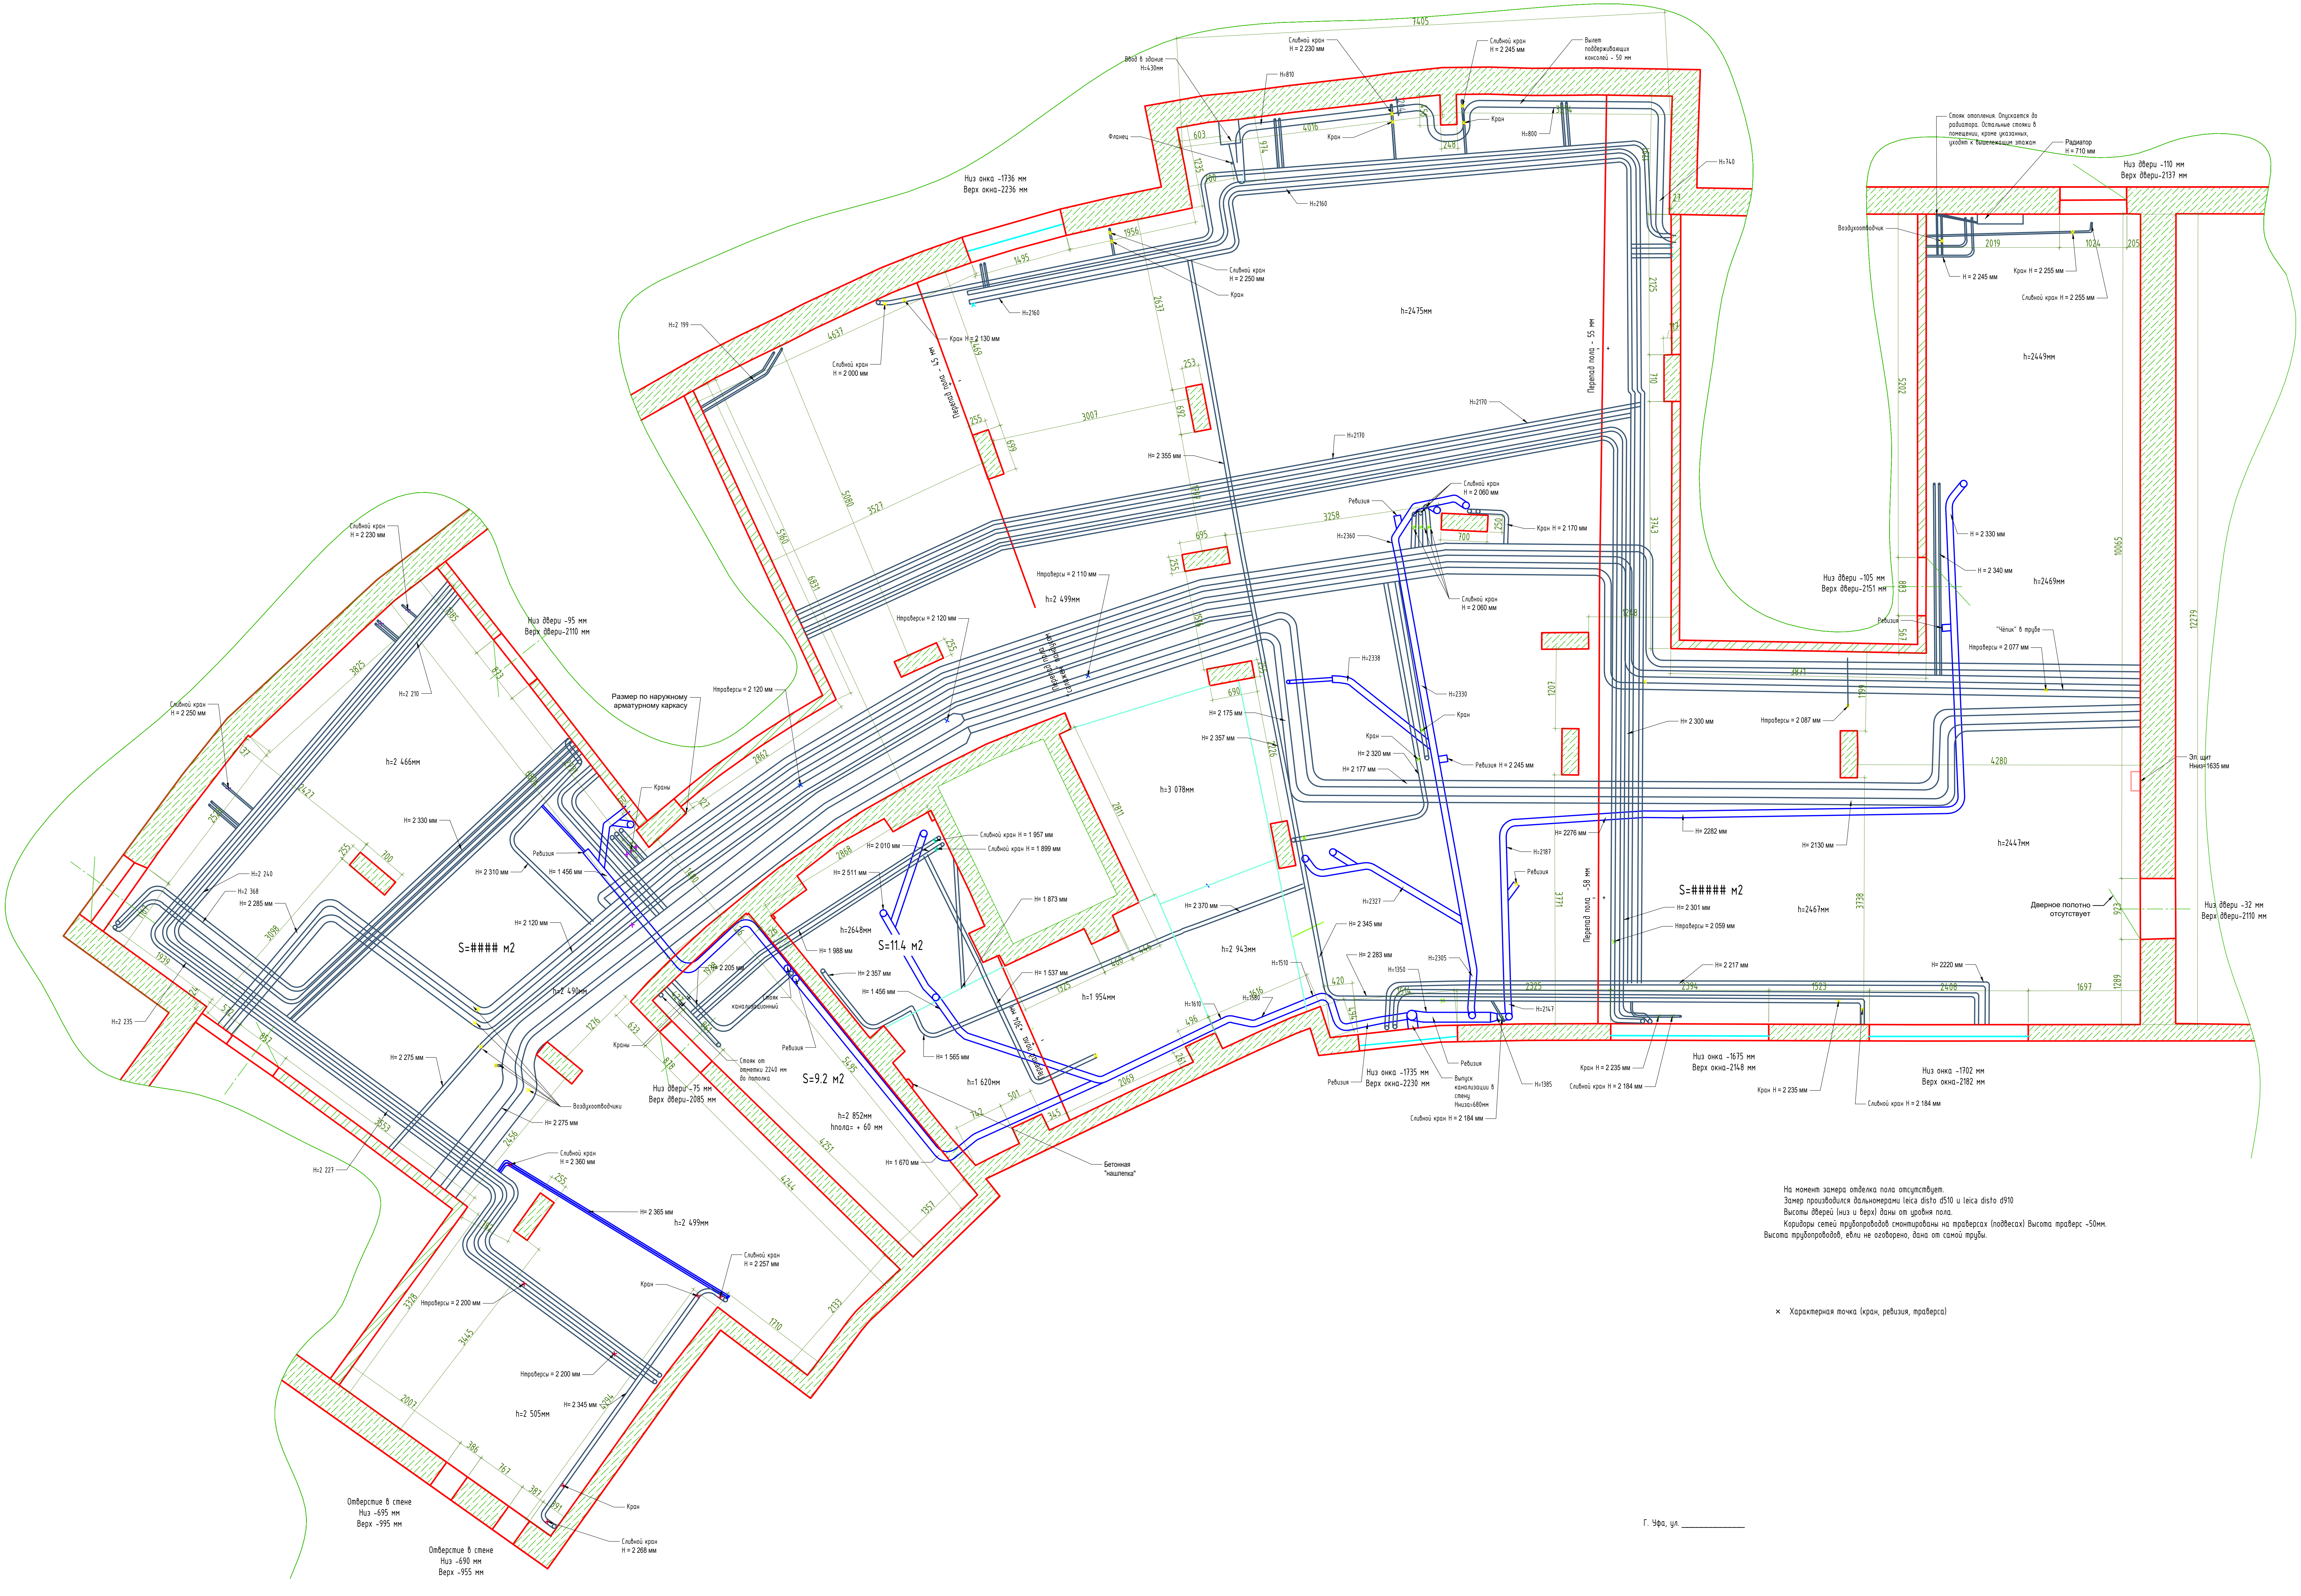

На момент замера отделка пола отсутствует.
Замер производился дальномерами leica disto d510 и leica disto d910
Высоты дверей (низ и верх) даны от уровня пола.
Коридоры сетей трубопроводов смонтированы на траверсах (подвесах) Высота траверс ~50мм.
Высота трубопроводов, евли не оговорено, дана от самой трубы.

× Характерная точка (кран, ревизия, траверса)

Г. Уфа, ул. ______________